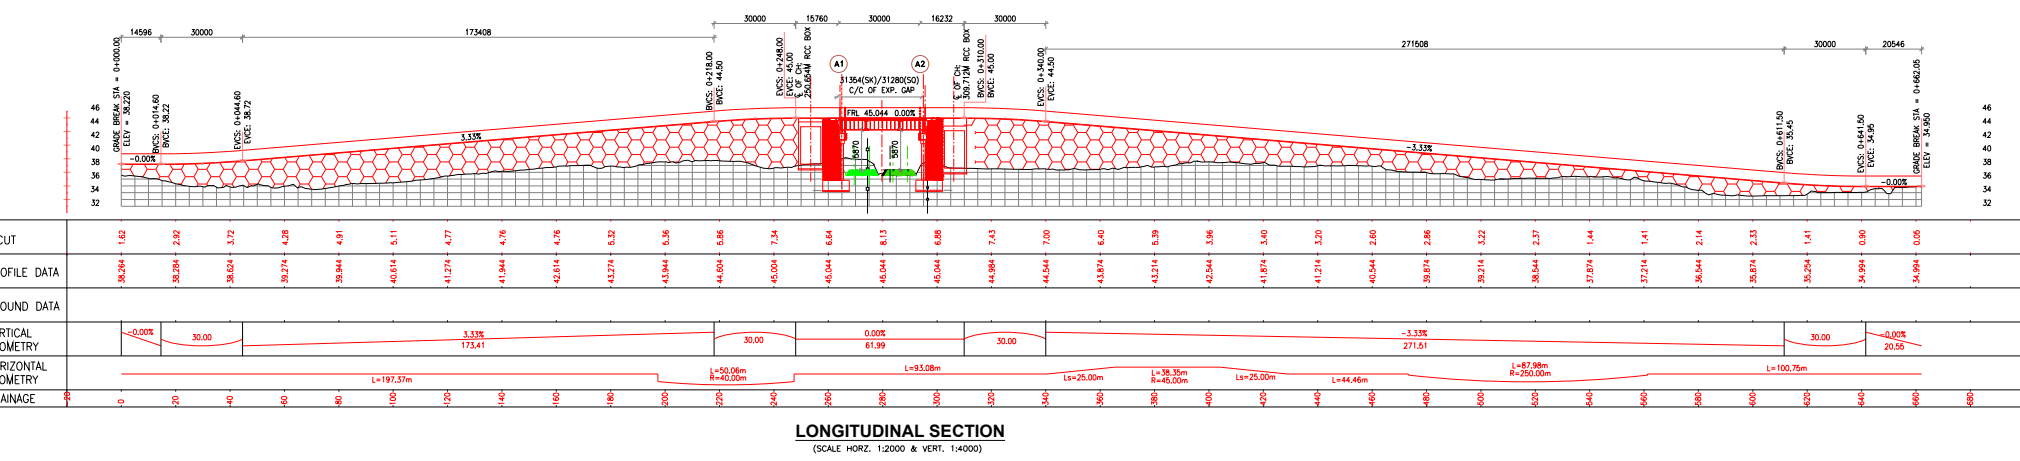
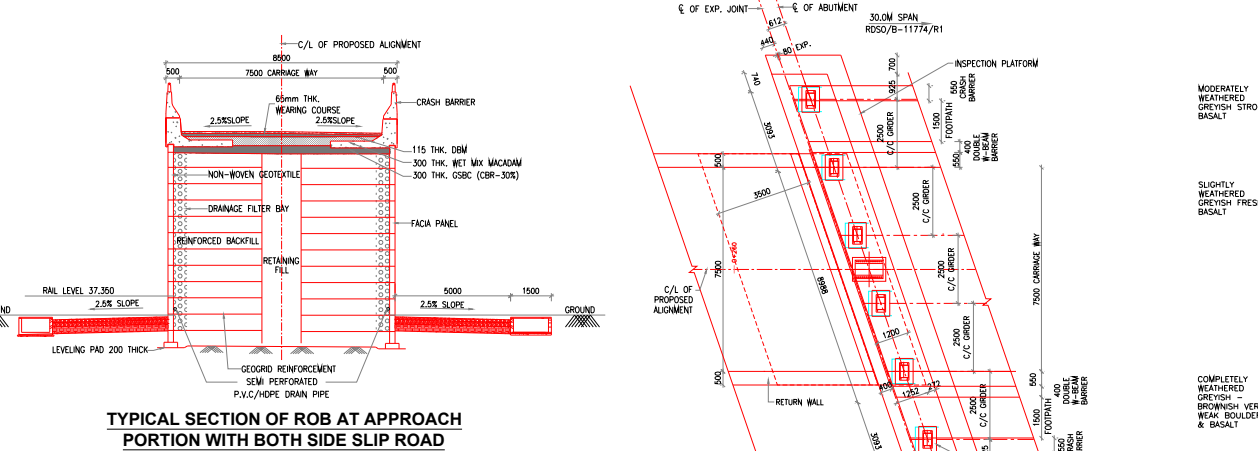
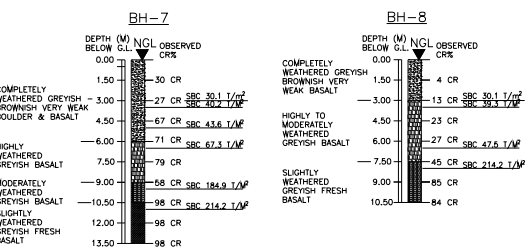
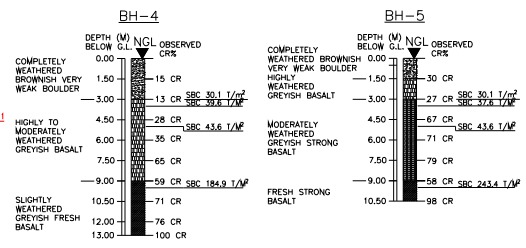
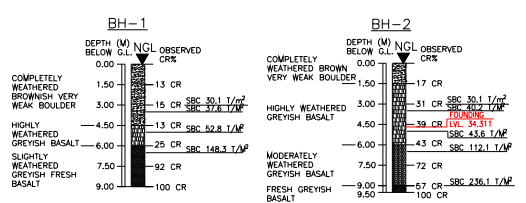
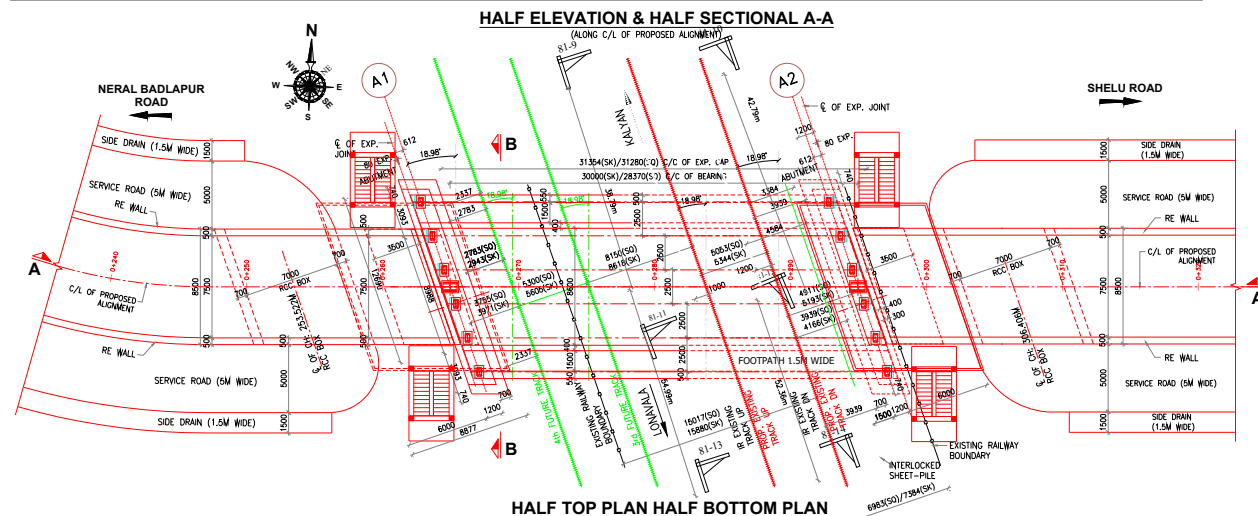
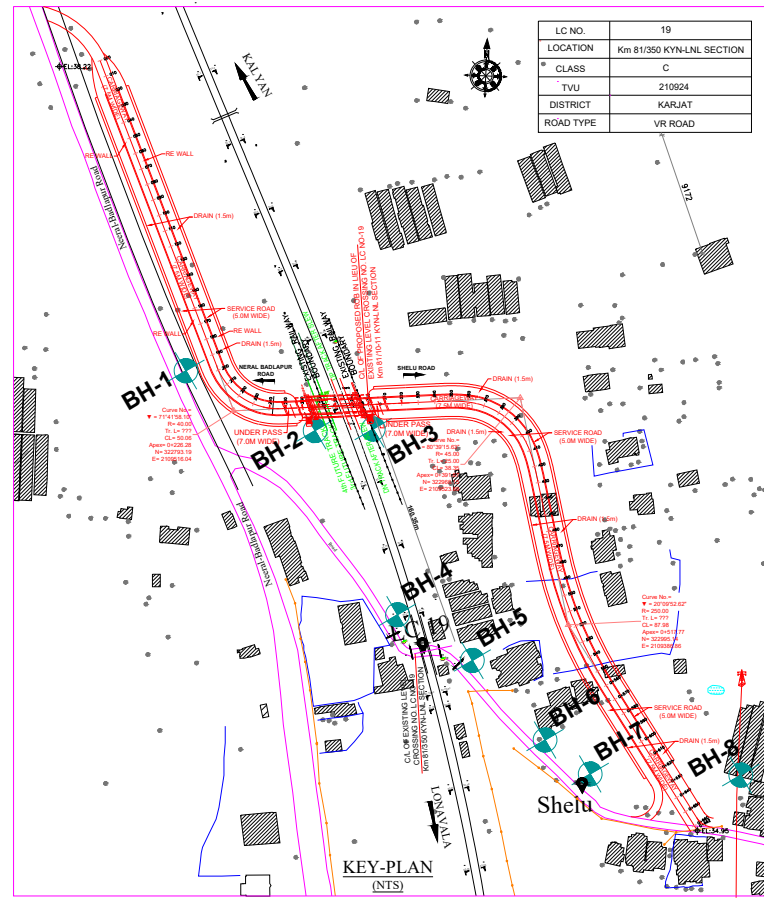
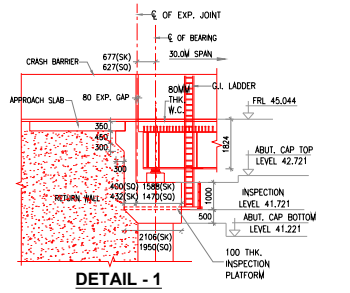
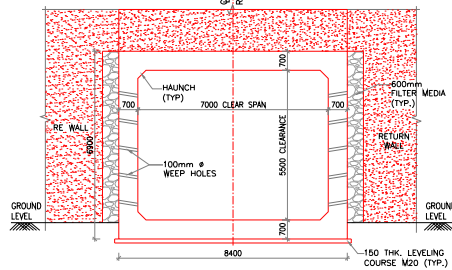
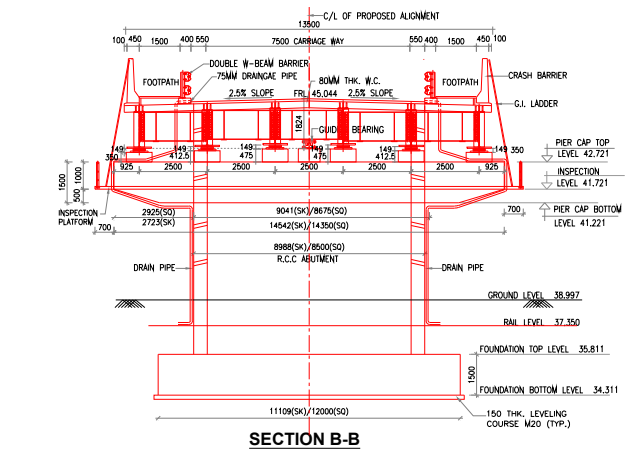


APPROVAL OF GENERAL ARRANGEMENT DRAWING	
HQ APPROVAL	
DESIGNATION	SIGNATURE
CBE	
DY.CE BR-I	
SSE-ROB-RUB-HQ	

DIVISION APPROVAL	
DRM	Digitally signed by HIRSHI MANA Date: 2025.05.30 21:36:18 +05'30'
ADMN-INFRA	Digitally signed by ANOESHI VERMA Date: 2025.05.23 13:40:59 +05'30'
SR.DDM(CO)	Digitally signed by ASHOK SINGH RAJPAKSHA Date: 2025.05.16 18:03:01 +05'30'
SR.DEE(G)	Digitally signed by GAUTAM KUMAR Date: 2025.05.15 11:21:55 +05'30'
SR.DEE(G)	Digitally signed by SHWETI LAL Date: 2025.05.15 17:45:13 +05'30'
SR.DEE(TO)	Digitally signed by DEEPAK KUMAR Date: 2025.05.06 16:16:03 +05'30'
SR.DSTE	Digitally signed by ALOK KUMAR Date: 2025.05.09 17:30:12 +05'30'
SR.DEN	Digitally signed by MD NAZULHAJ Date: 2025.05.14 10:37:55 +05'30'

CONSTRUCTION APPROVAL	
CE/C/RSP	Digitally signed by ARBIND KUMAR SINGH Date: 2025.06.02 14:21:47 +05'30'
DY.CE/C/GC	Digitally signed by AMRIT ANAND Date: 2025.05.23 11:36:27 +05'30'
DY.CE/C/RSP	Digitally signed by PREETA KUMARI Date: 2025.04.24 13:40:08 +05'30'
AXEN/C/RSP	Digitally signed by SHAMUKHASTASTRY ANGALAKUTTI Date: 2025.04.04 11:33:57 +05'30'
SSE/D&D/C/RSP	Digitally signed by ASHUTOSH CHAUHAN Date: 2025.04.03 19:37:05 +05'30'

CONSULTANT - RITES Ltd.		
DESIGNATION		SIGNATURE
APPROVED BY	GM/CEDS	
CHECKED BY	JGM/CEDS	
DESIGN BY	Sr. Mgr/CEDS	
	AM/CEDS	
PREPARED BY	TECH. GRADE II	

LOADING STANDARD	IRC-6 2017 SEISMIC ZONE - III
 CENTRAL RAILWAY	
GENERAL ARRANGEMENT DRAWING	
DIVISION	MUMBAI
SECTION	KALYAN-LONAVALA (KYN-LNL)
EXECUTIVE AGENCY	RSP UNIT, CENTRAL RAILWAY
CONSULTANT	 RITES Limited (A Government of India Enterprise) RITES Bhawan, Plot No. 1, Sector-28 Gurgaon-122001, Haryana (India)
PROJECT	DETAILED DESIGN CONSULTANCY SERVICES FOR CONSTRUCTION OF 15 ROAD OVER BRIDGES, GATT SHAKTI UNIT OF MUMBAI DIVISION OF CENTRAL RAILWAY. PB ITEM NO. 218 OF 2020-21
DRAWING TITLE	CONSTRUCTION OF ROB AT KM: 61/10-11 IN LIEU OF RL-19 AT KM: 61/350 BETWEEN VANGANTI-SHELU RLY. STATION ON KALYAN-LONAVALA SECTION (ON NERAL BALFUR ROAD-SHELU ROAD) SPAN: 1x30m C.G.
DRAWING NO.	CONSULTANT: RITES/UCDS/RSP-MUMBAI/ROB-19/GAD. CONSTRUCTION: GMR/ESP-1004-ROB HEAD QUARTER:
SCALE:	1:200 & 1:100