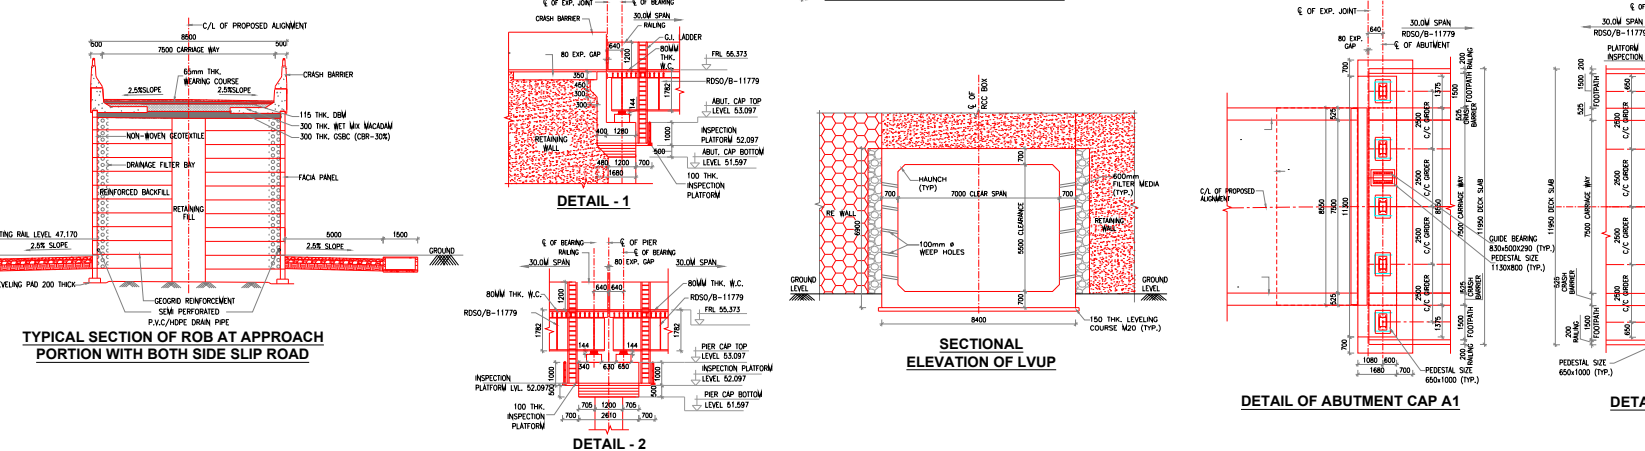
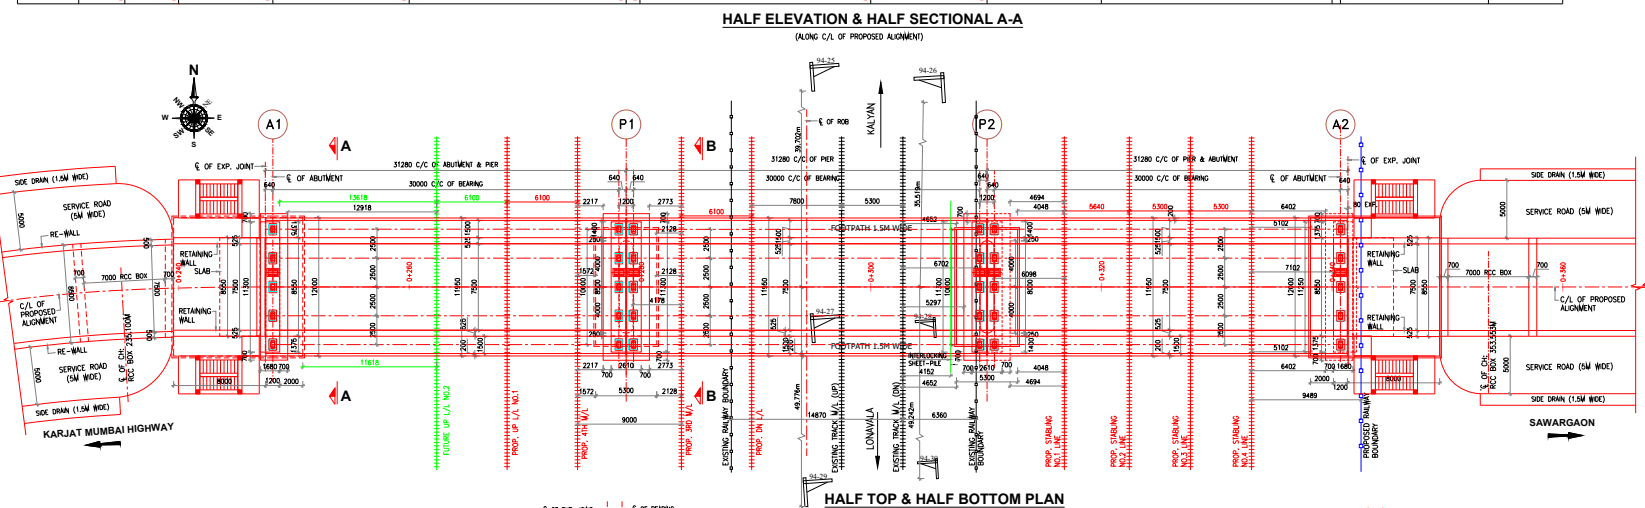
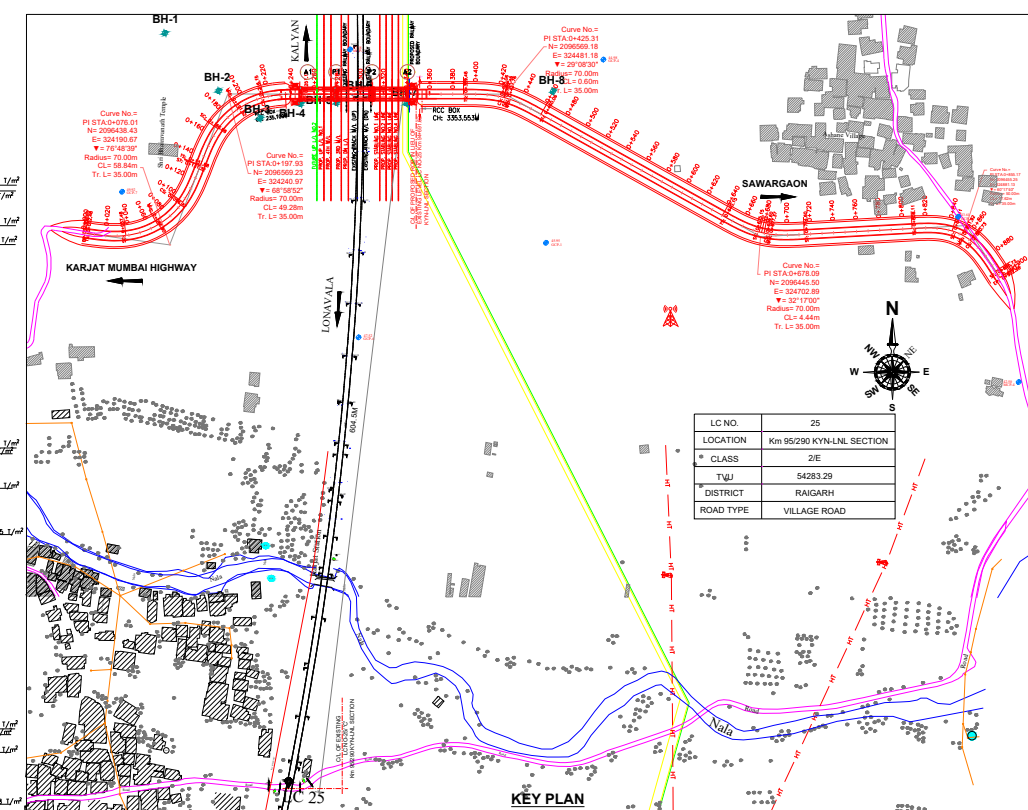
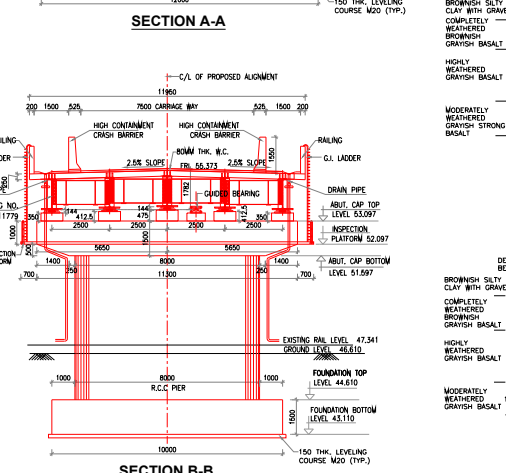
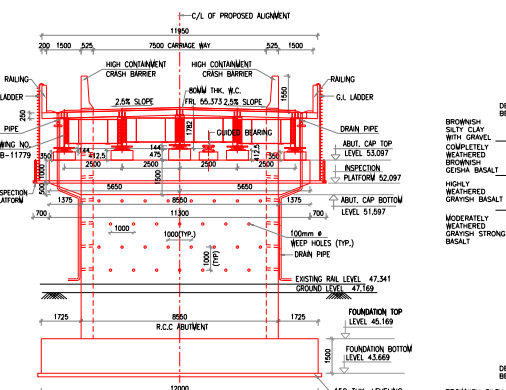


| APPROVAL OF GENERAL<br>ARRANGEMENT DRAWING |           |
|--------------------------------------------|-----------|
| HQ APPROVAL                                |           |
| DESIGNATION                                | SIGNATURE |
| CSE                                        |           |
| DT,CE BR-1                                 |           |
| EE,POE,BR-10                               |           |

| DIVISION APPROVAL |                                                                             |
|-------------------|-----------------------------------------------------------------------------|
| DPM               | Digitally signed by HIRSHU KHAN<br>Date: 2025.07.08 21:52:50 +05'30'        |
| ADMN              | Digitally signed by NARAIN KUMAR<br>Date: 2025.07.07 18:55:32 +05'30'       |
| SR.DWM(CO)        | Digitally signed by ROSHI DIXIT/PAI PM<br>Date: 2025.06.20 19:04:41 +05'30' |
| SR.DCM(CO)        | Digitally signed by GAURAV KUMAR<br>Date: 2025.06.15 12:15:43 +05'30'       |
| SR.DEE(C)         | Digitally signed by SHANU LAL<br>Date: 2025.06.15 18:44:24 +05'30'          |
| SR.DEE(TD)        | Digitally signed by DEEPAKASH SINGH<br>Date: 2025.06.08 17:39:44 +05'30'    |
| SR.DSE            | Digitally signed by ALOK KUMAR<br>Date: 2025.06.22 15:56:59 +05'30'         |
| SR.DITE           | Digitally signed by MD NAJIBULLAH<br>Date: 2025.06.22 15:56:59 +05'30'      |

| CONSTRUCTION APPROVAL |                                                                                          |
|-----------------------|------------------------------------------------------------------------------------------|
| CE/C/RSP              | Digitally signed by ARBINO KUMAR<br>Date: 2025.07.10 10:50:22 +05'30'                    |
| DY.CE/C/GC            | Digitally signed by AJAY ANAND<br>Date: 2025.07.04 18:39:09 +05'30'                      |
| DY.CE/C/RSP           | Digitally signed by REETA KUMAR<br>Date: 2025.02.24 11:58:56 +05'30'                     |
| ANEN/C/RSP            | Digitally signed by SIVAKUMARASASTRI<br>ANGARAKUTTI Date: 2025.02.24<br>10:40:43 +05'30' |
| SSE/D&D/C/RSP         | Digitally signed by ASHUTOSH CHAKRA<br>Date: 2025.02.21 09:56:08 +05'30'                 |

| CONSULTANT - RITES Ltd. |                |                                                                                       |
|-------------------------|----------------|---------------------------------------------------------------------------------------|
| DESIGNATION             |                | SIGNATURE                                                                             |
| APPROVED BY             | GM/CEDS        |  |
| CHECKED BY              | JGM/CEDS       |  |
| DESIGN BY               | Sr. Wpr/CEDS   |  |
| PREPARED BY             | AM/CEDS        |  |
| PREPARED BY             | TECH. GRADE II |  |

|                             |   |
|-----------------------------|---|
| LOADING<br>STANDARD         | ISO - 6 2017<br>SEISMIC ZONE - III   |
| CENTRAL RAILWAY             |   |
| GENERAL ARRANGEMENT DRAWING |   |
| DIVISION                    | MUMBAI   |
| SECTION                     | KALANJ-LONAYANA (KYN-LNL)   |
| EXECUTIVE AGENCY            | RSP UNIT, CENTRAL RAILWAY   |
| CONSULTANT                  |  <b>RITES Limited</b><br>1015, 1016, 1017, 1018,1 |