
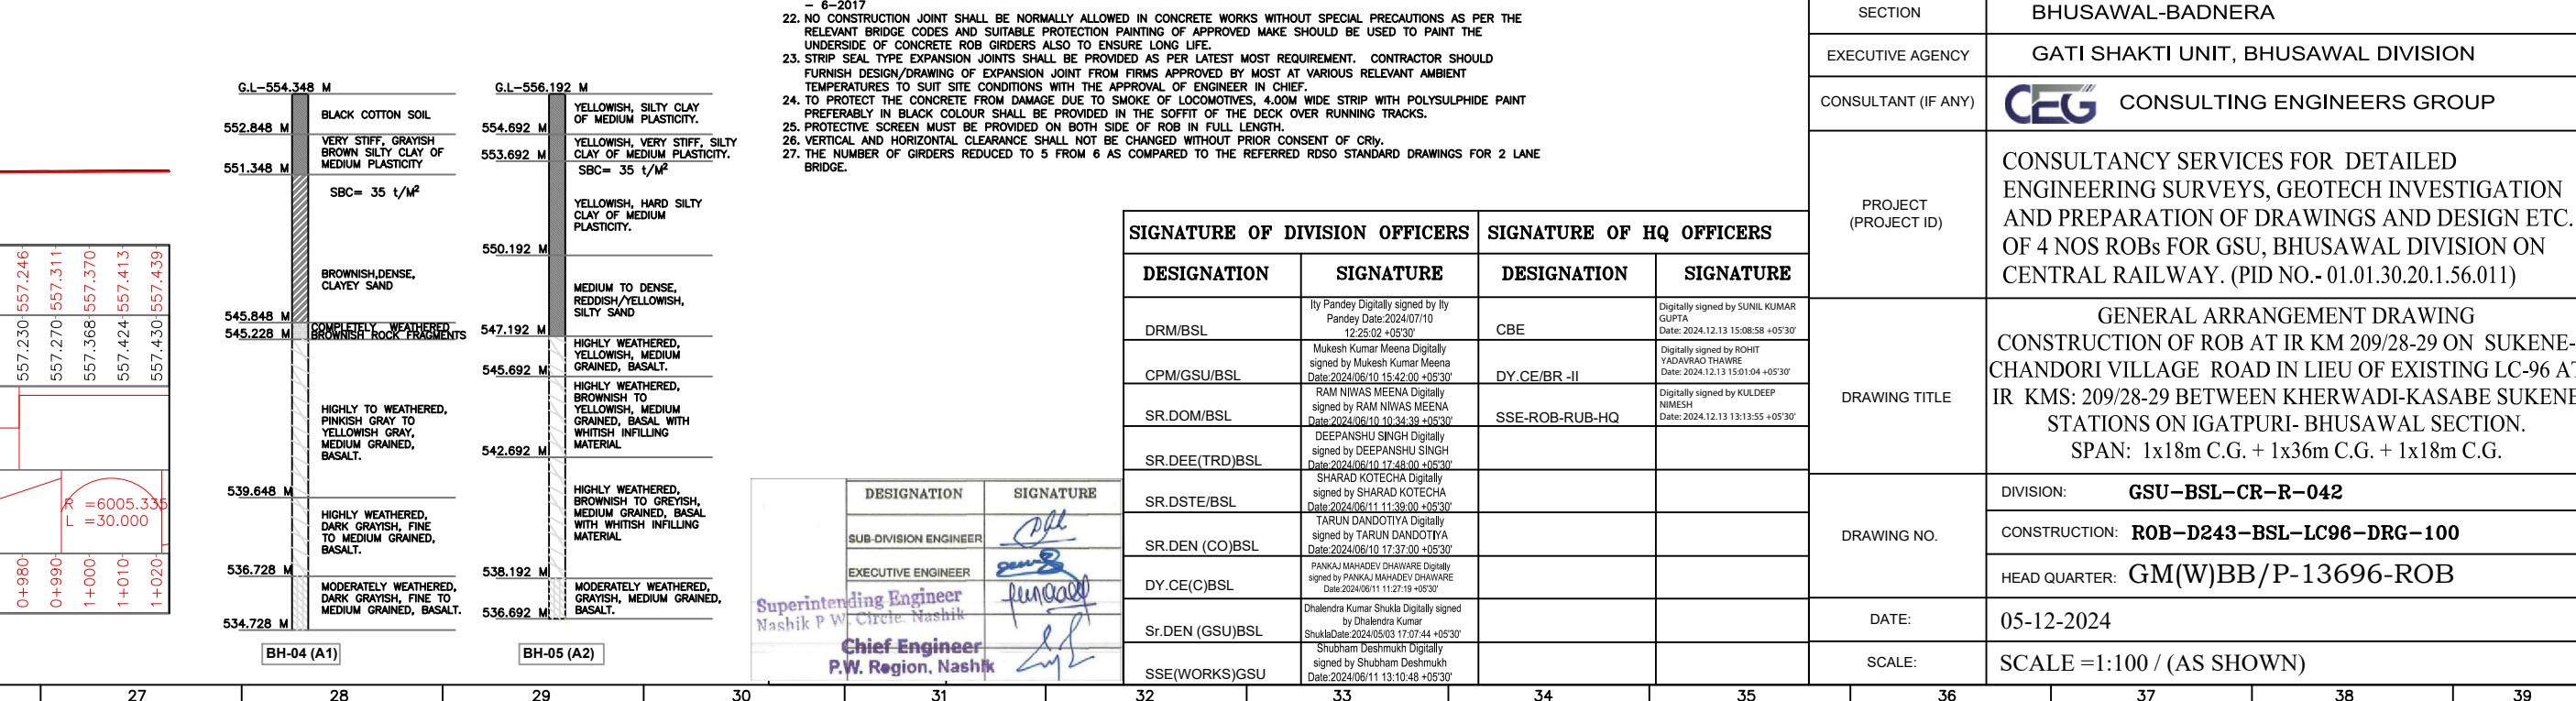
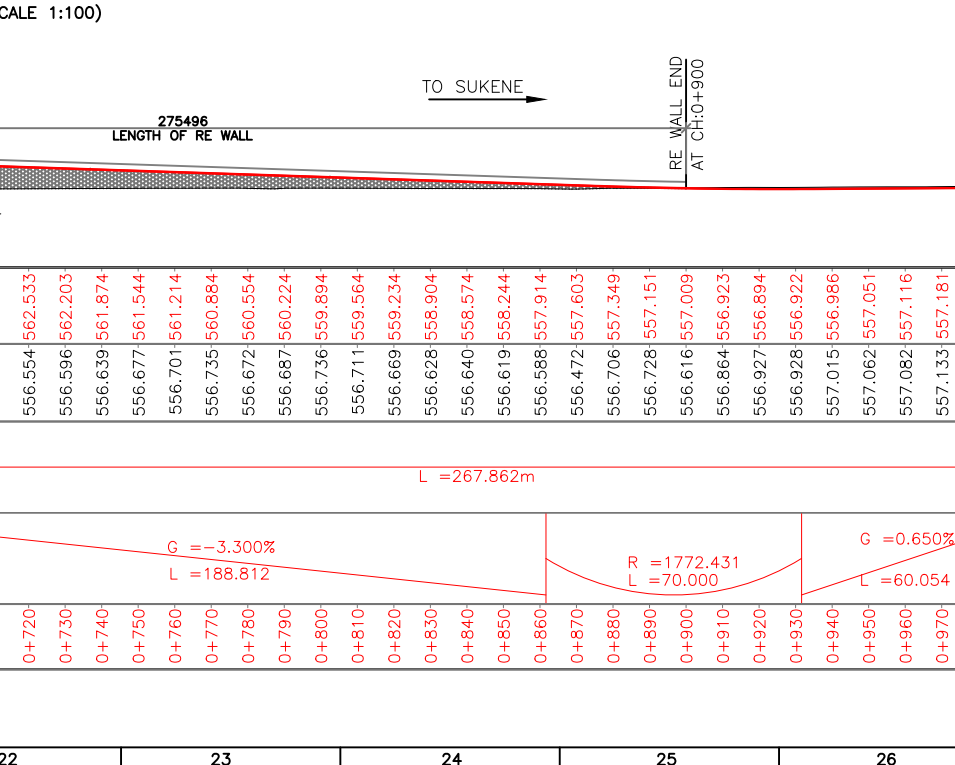
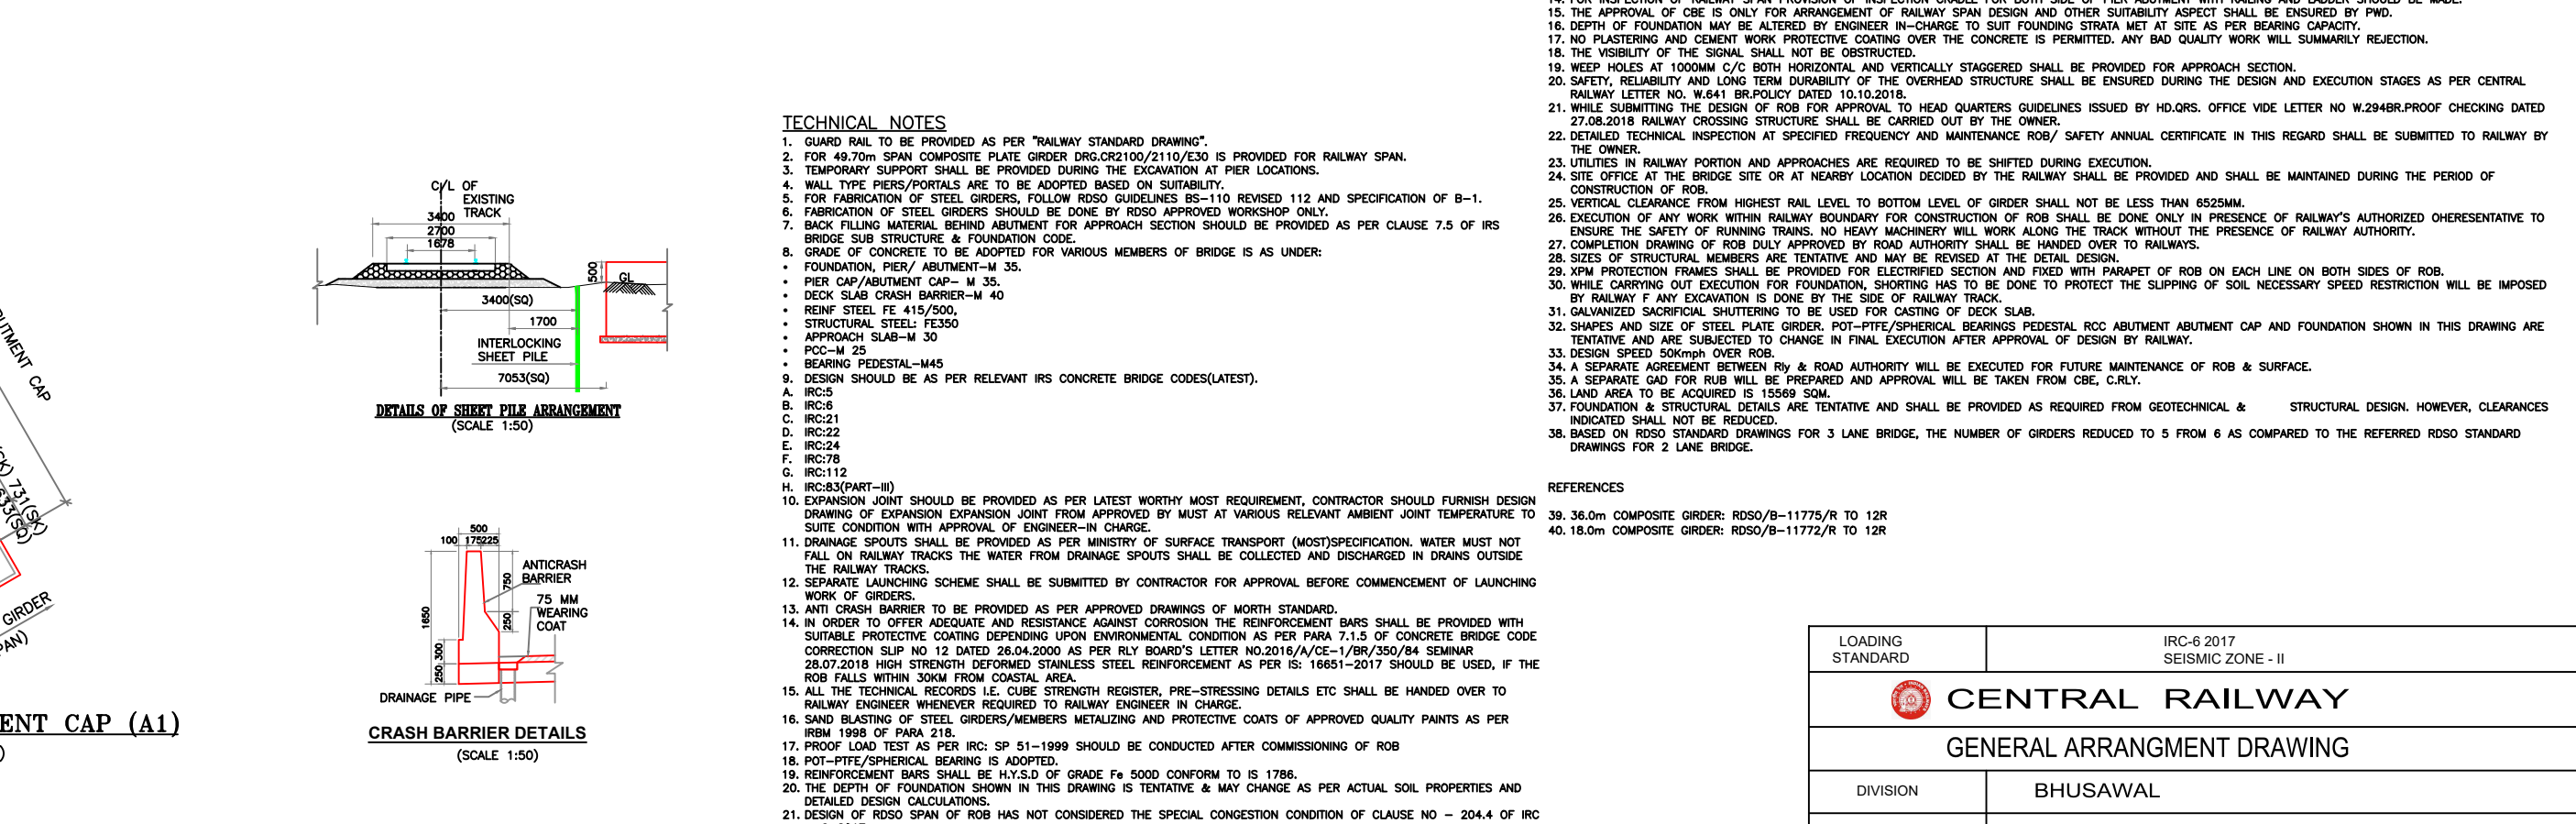
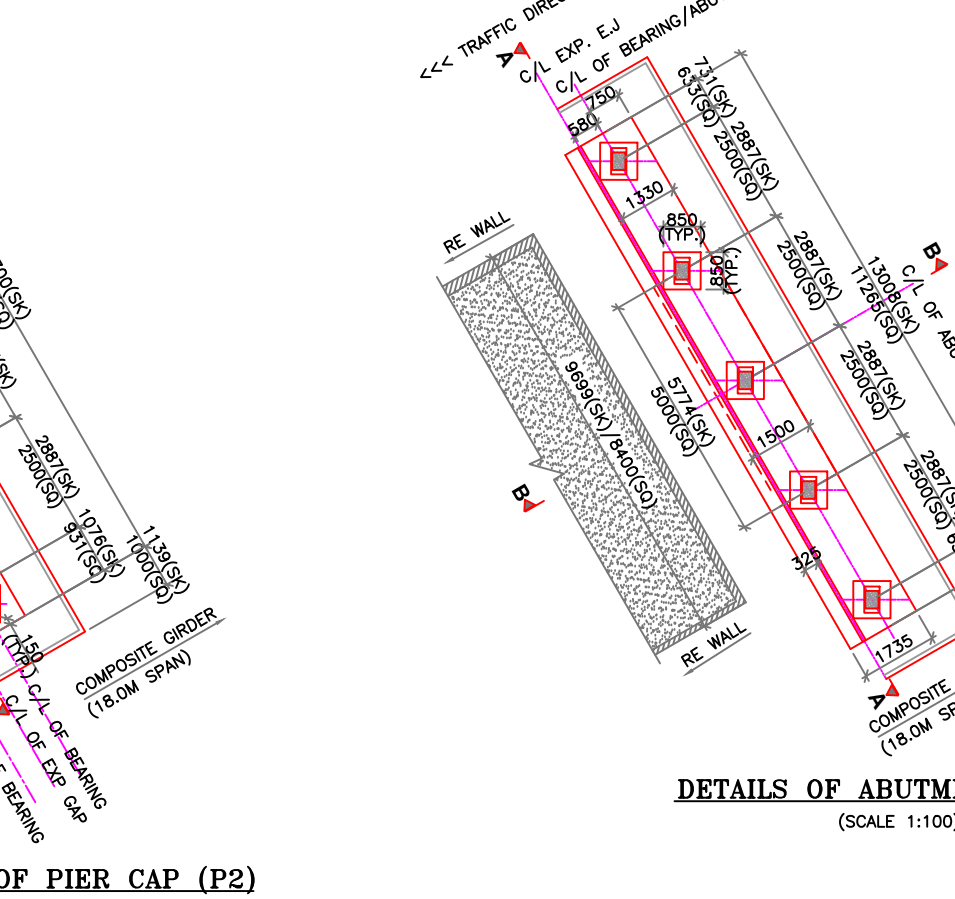
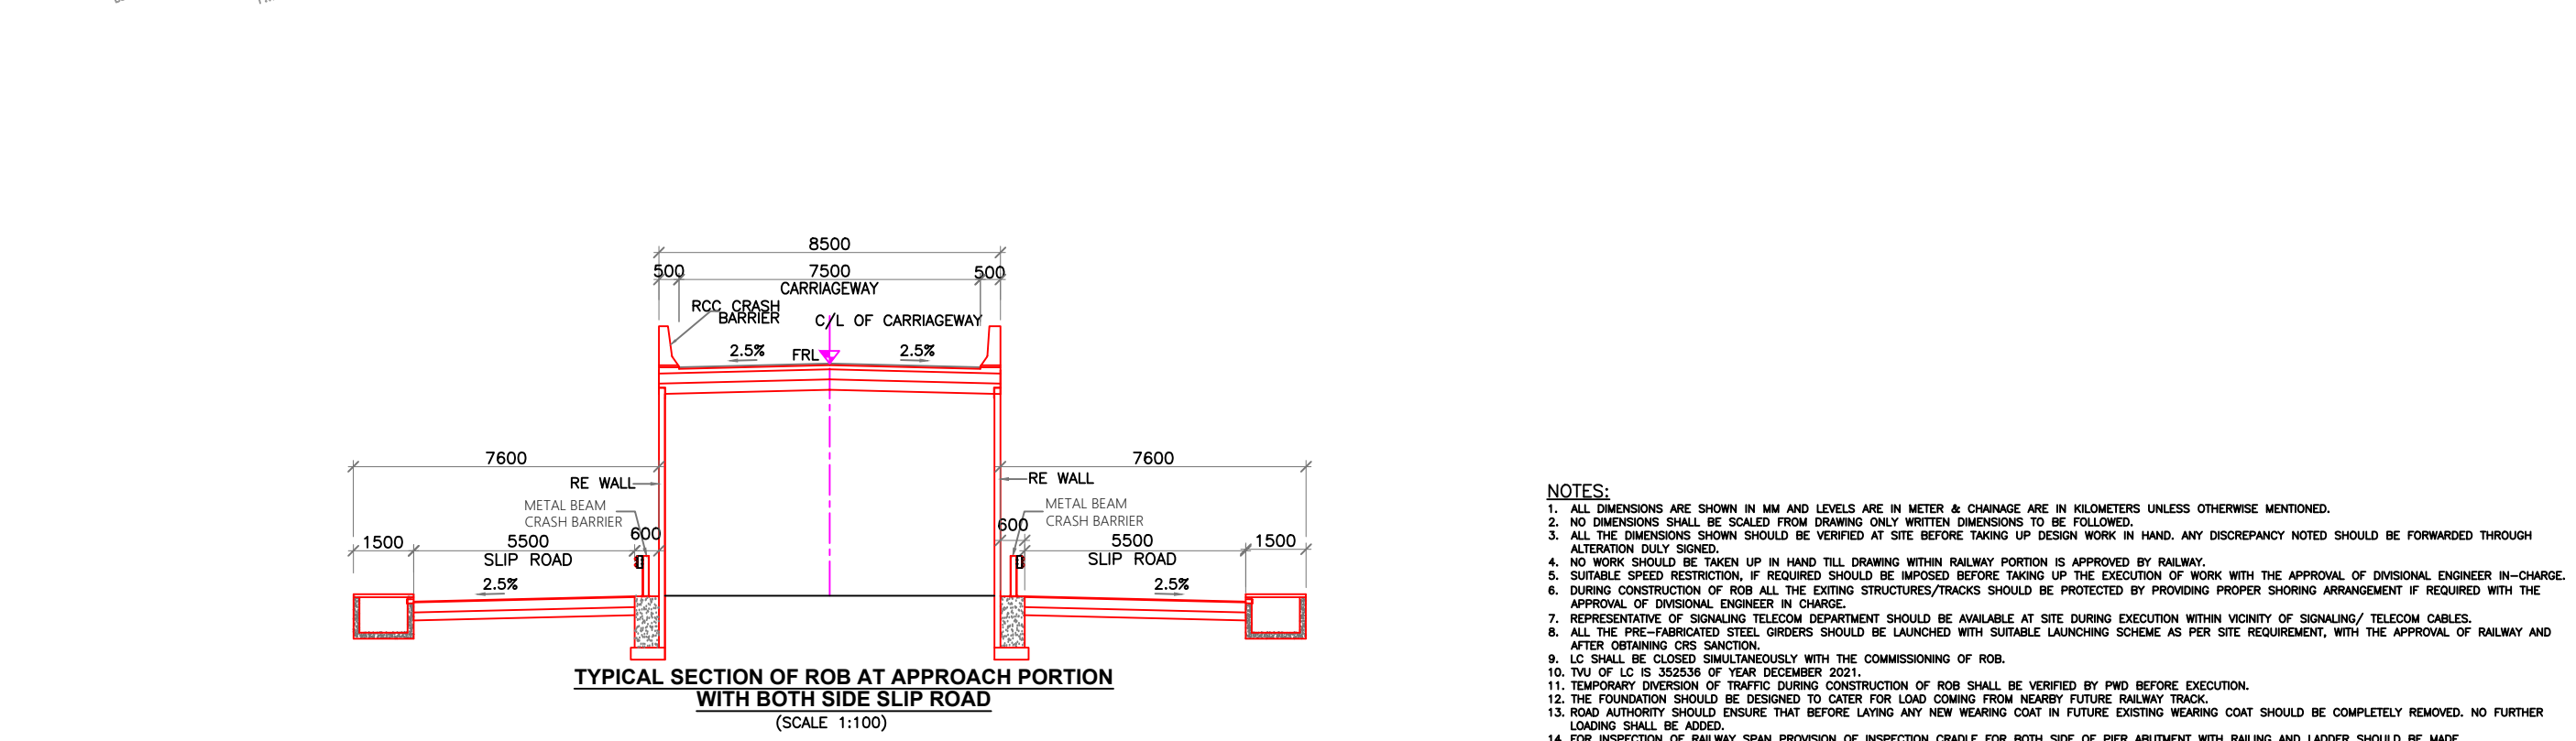
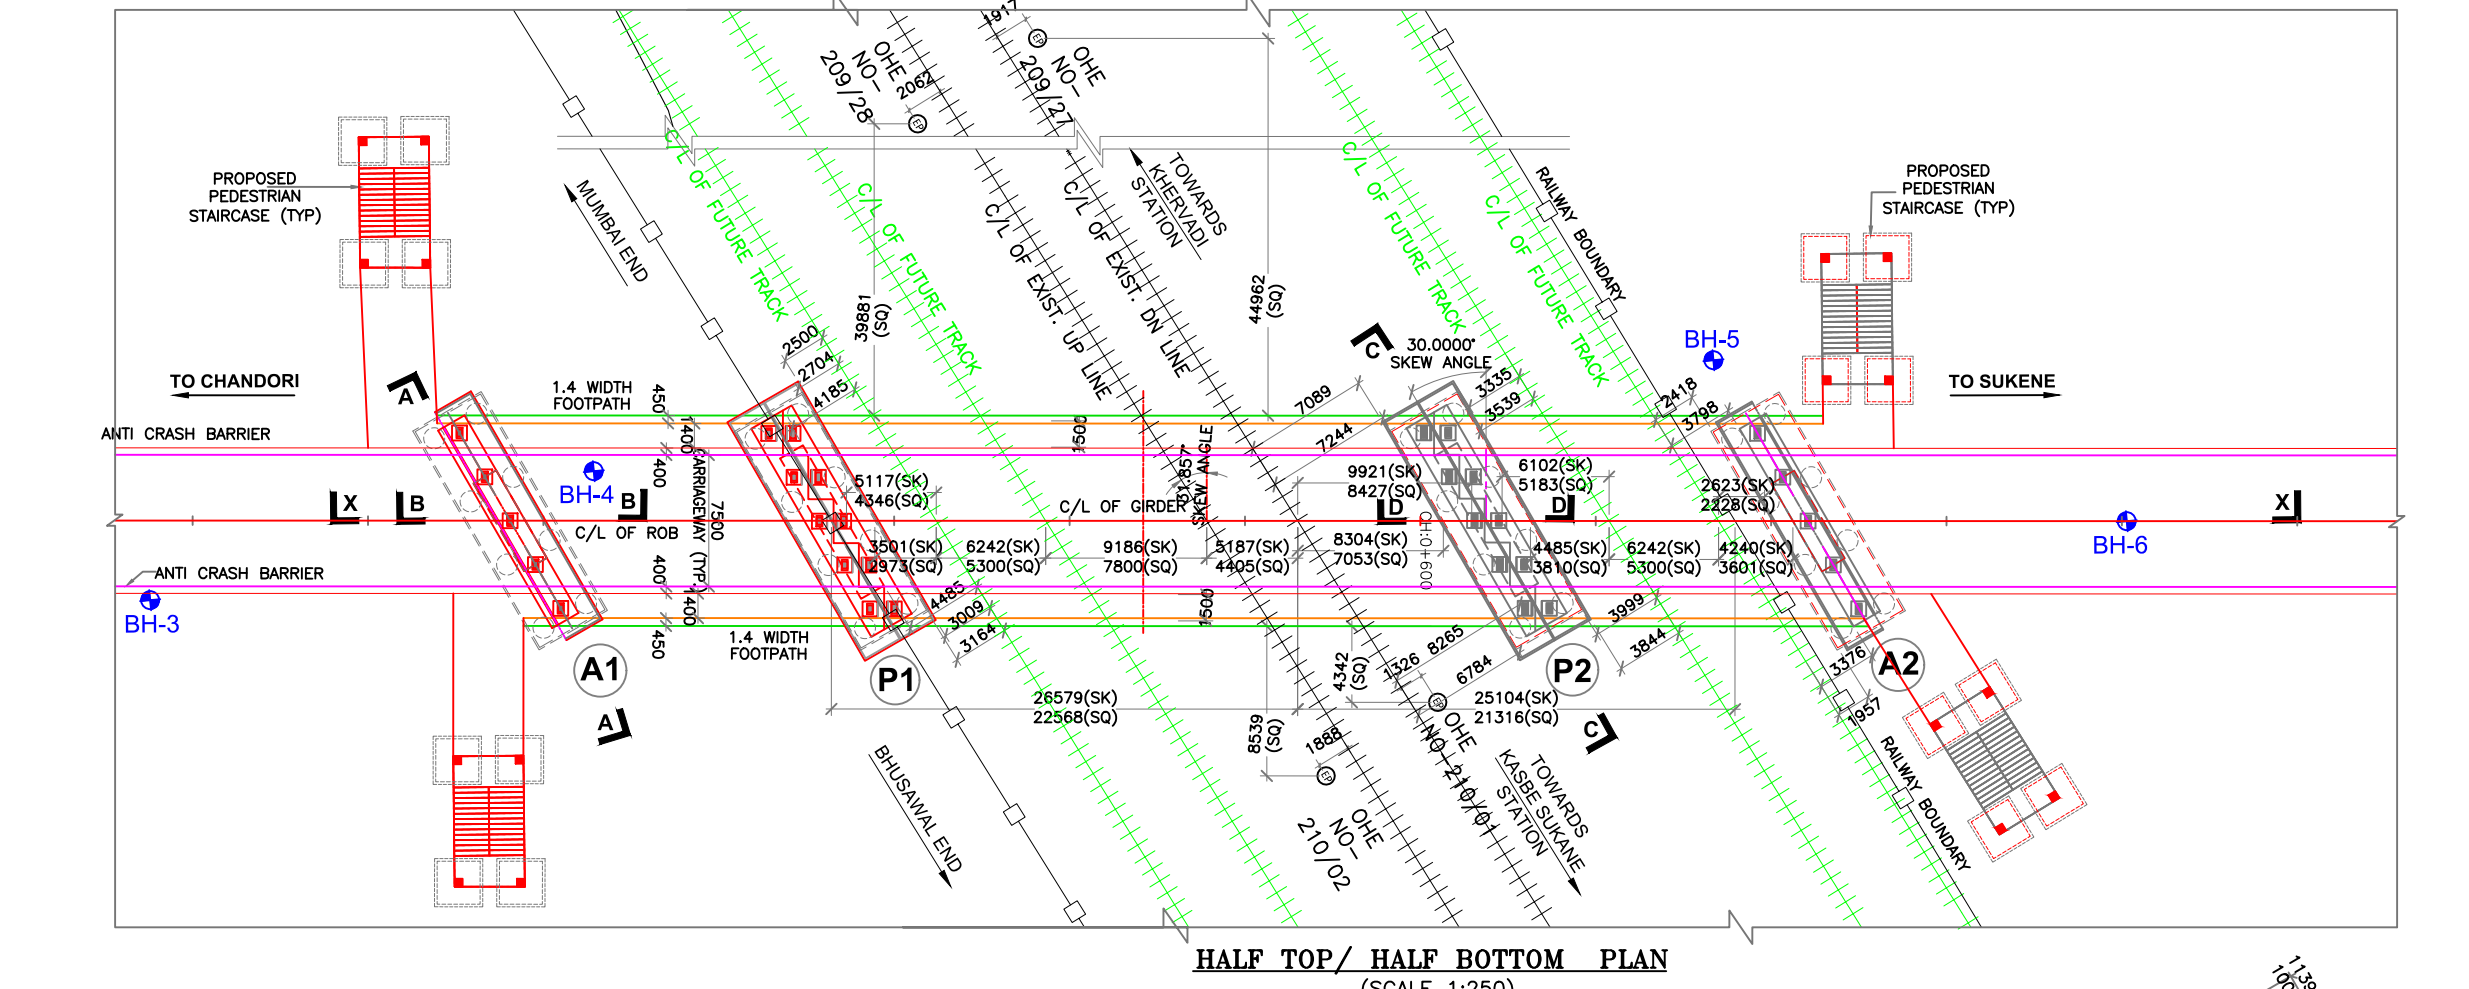


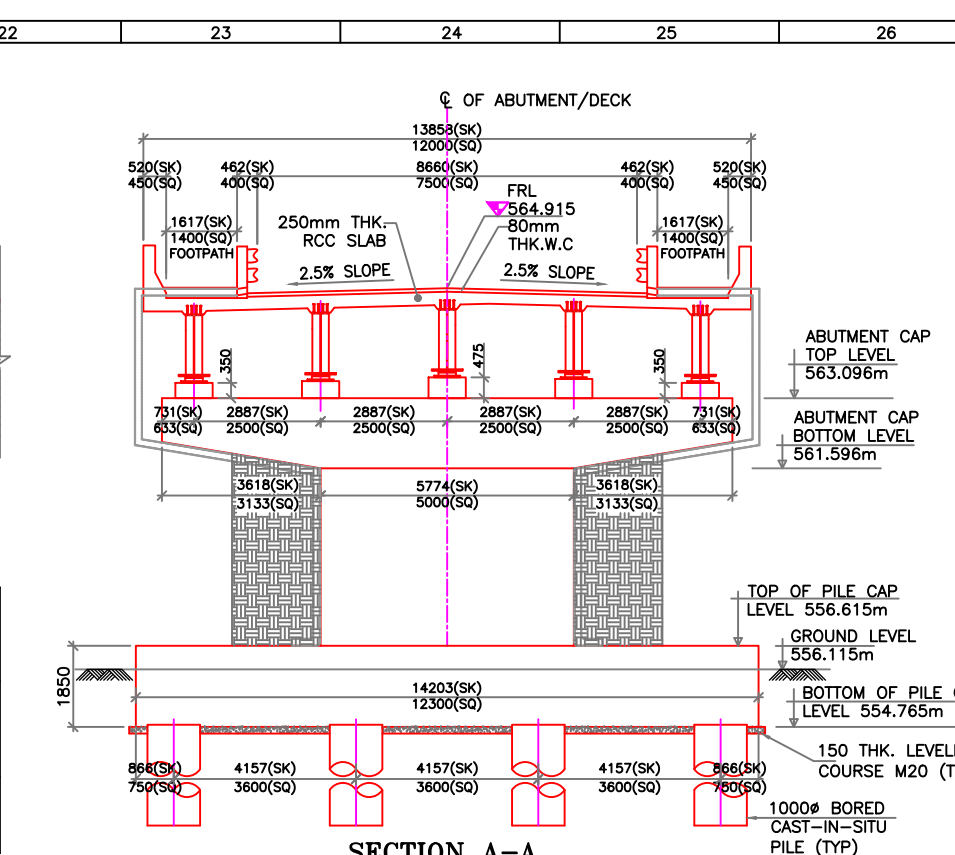

LOADING STANDARD		IRC-6 2017 SEBIMC ZONE - II
 CENTRAL RAILWAY		
GENERAL ARRANGMENT DRAWING		
DIVISION	BHUSAWAL	
SECTION	BHUSAWAL-BADNERA	
EXECUTIVE AGENCY	GATI SHAKTI UNIT, BHUSAWAL DIVISION	
CONSULTANT (IF ANY)	 CONSULTING ENGINEERS GROUP	
PROJECT (PROJECT ID)	CONSULTANCY SERVICES FOR DETAILED ENGINEERING SURVEYS, GOTECH INVESTIGATION AND PREPARATION OF DRAWINGS AND DESIGN ETC. OF 4 NOS ROBS FOR (SBL BHUSAWAL DIVISION ON CENTRAL RAILWAY, (PID NO.-01.01.30.201.56.011)	
DRAWING TITLE	GENERAL ARRANGMENT DRAWING CONSTRUCTION OF ROB AT IR KM 209/28-29 ON SUKENE- CHANDORI VILLAGE ROAD IN LIEU OF EXISTING LC-96 AT IR KMS: 209/28-29 BETWEEN KHERWADI-KASABE SUKENE STATIONS ON IGATPURI-BHUSAWAL SECTION, SPAN: 1x18 CM-C + 1x36 CM-C + 1x18m C.G.	
DRAWING NO.	DIVISION: GSU-BSL-CR-R-042 CONSTRUCTION: ROB-D243-BSL-LC96-DRG-100	
DATE:	HEAD QUARTER: GM(W)BB/P-13696-ROB 05-12-2024	
SCALE:	SCALE=1:100 / (AS SHOWN)	
	36	37
	38	39