
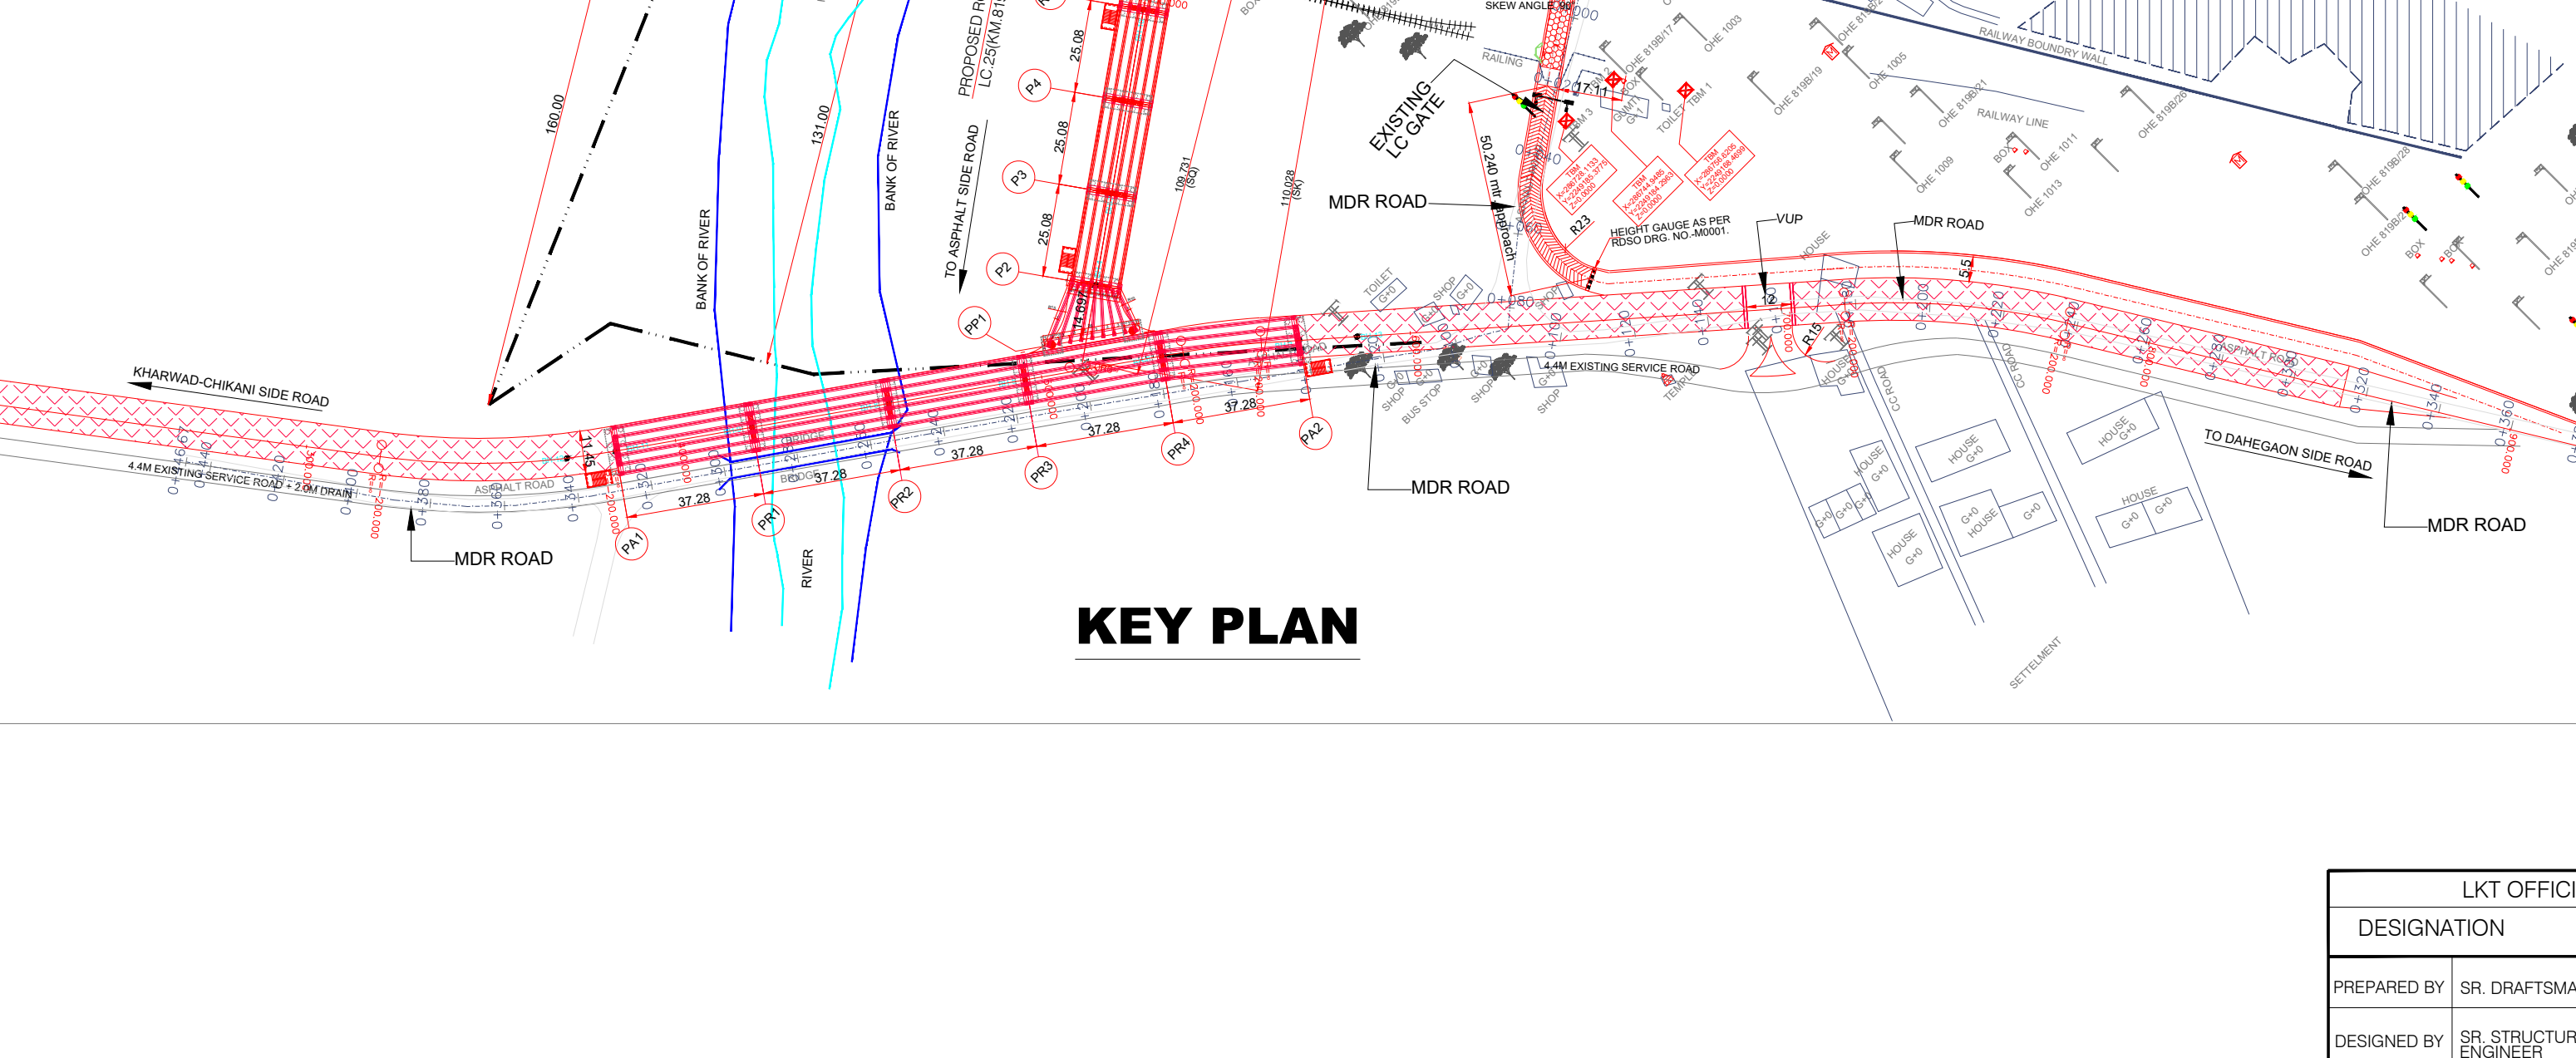
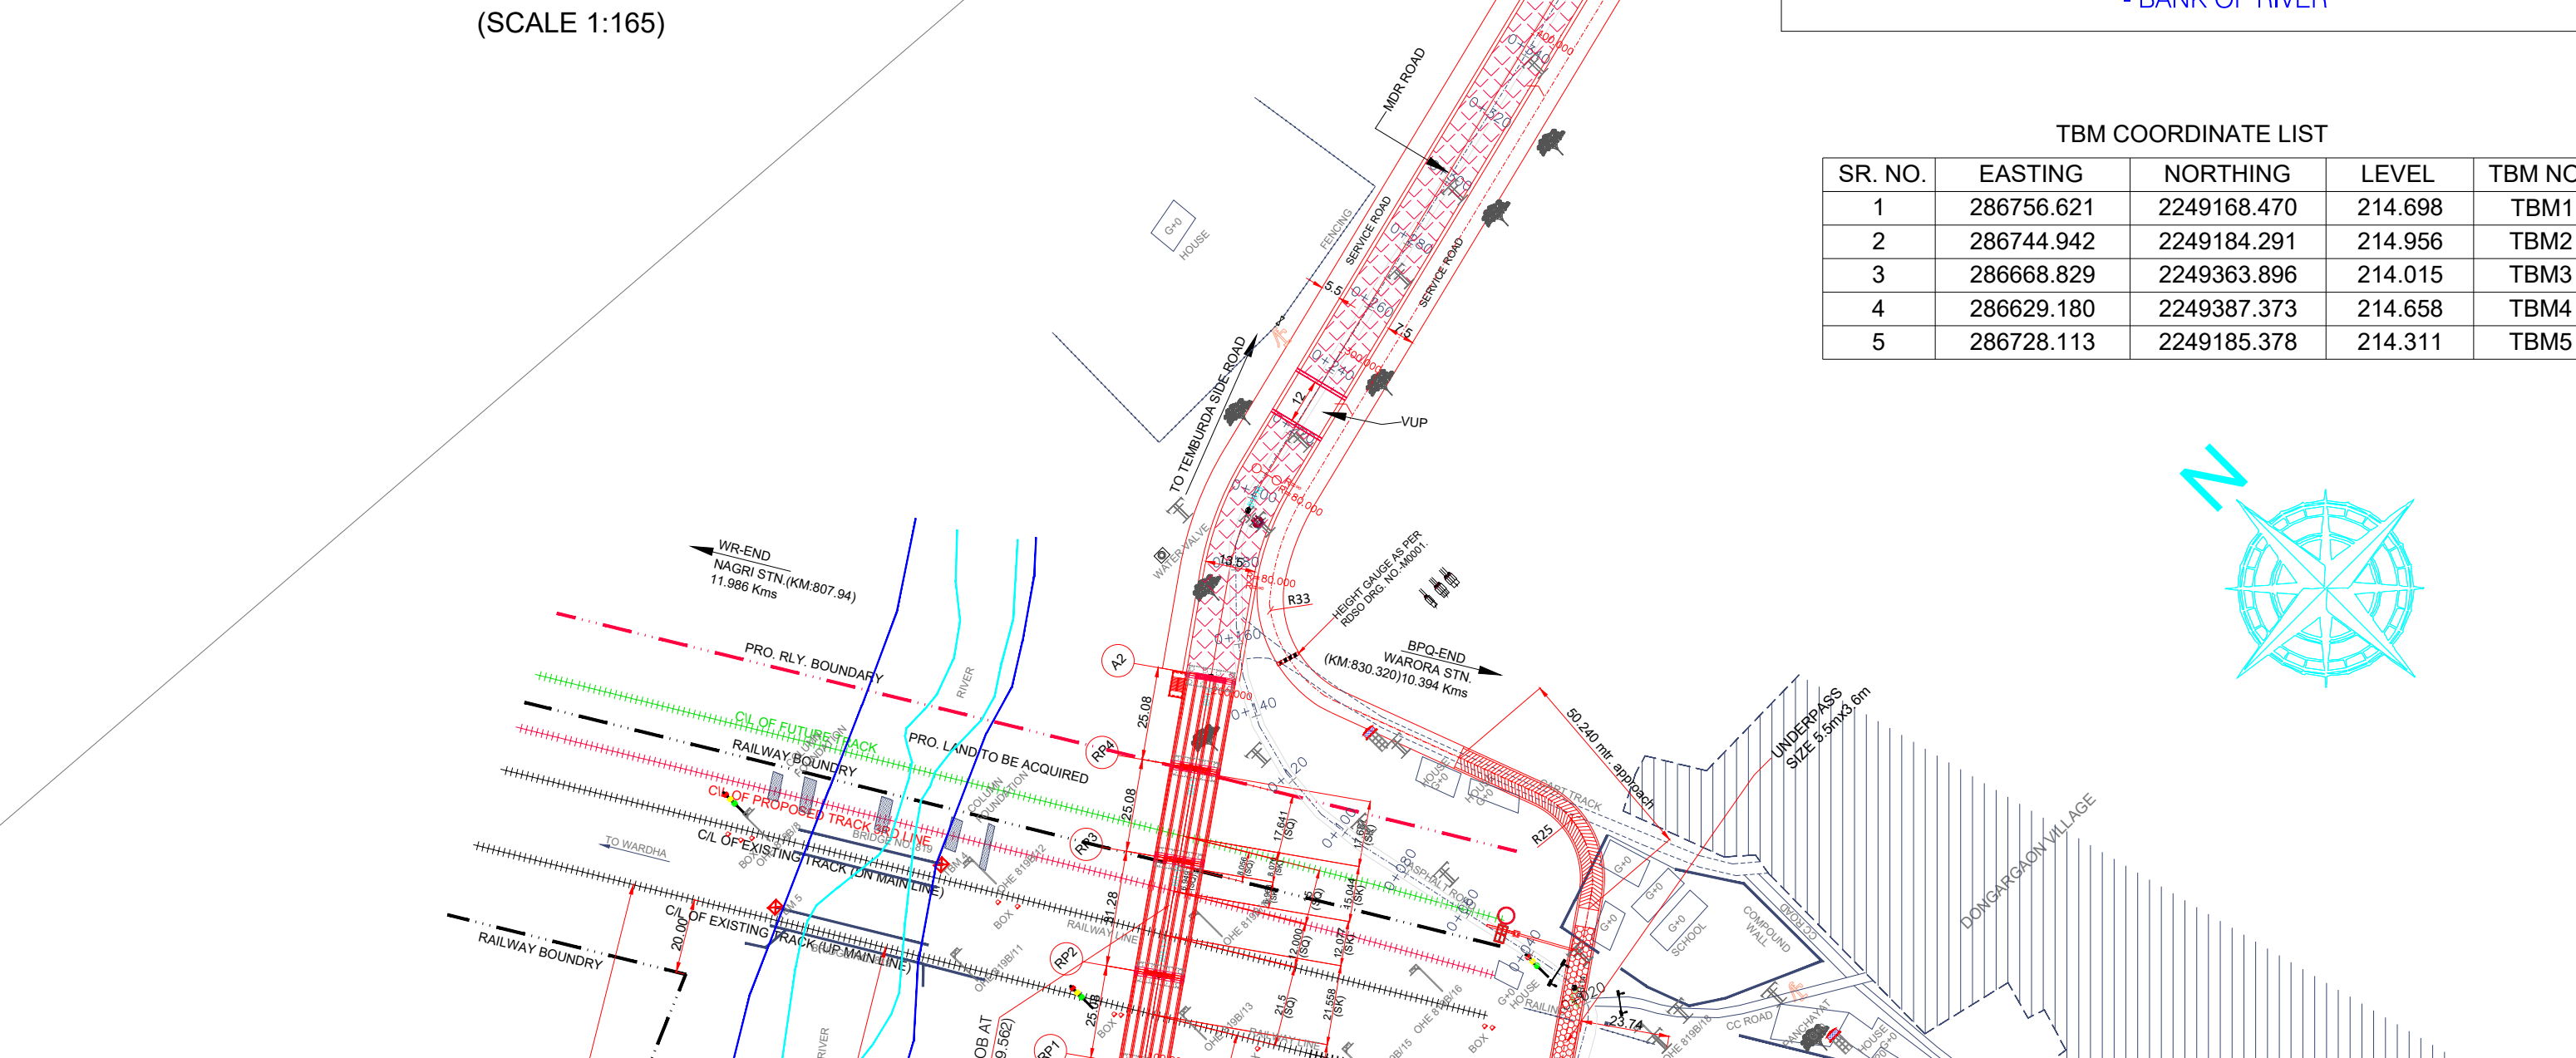
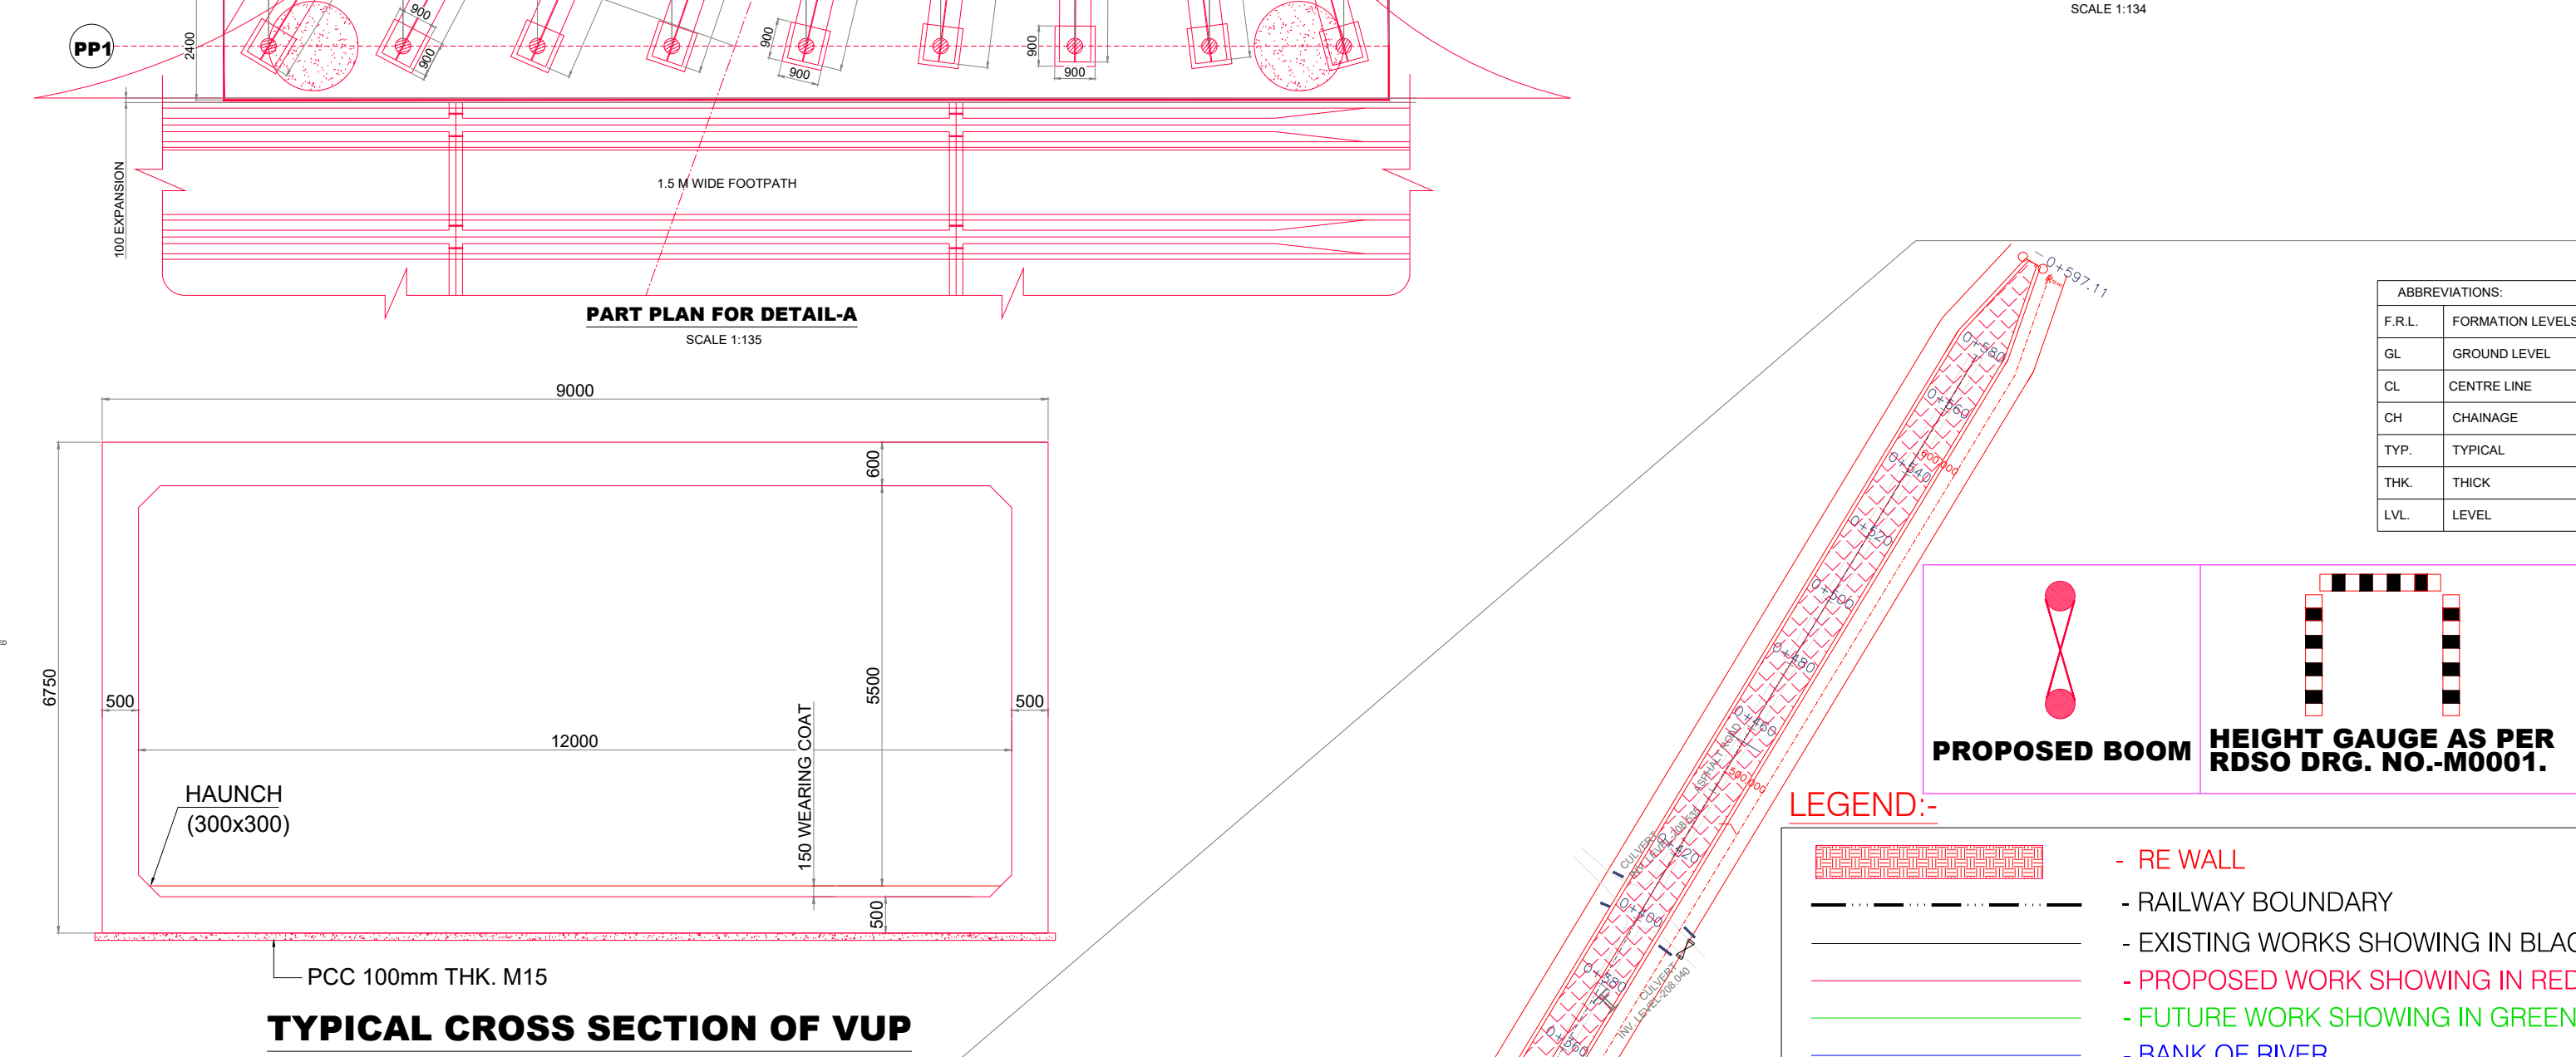


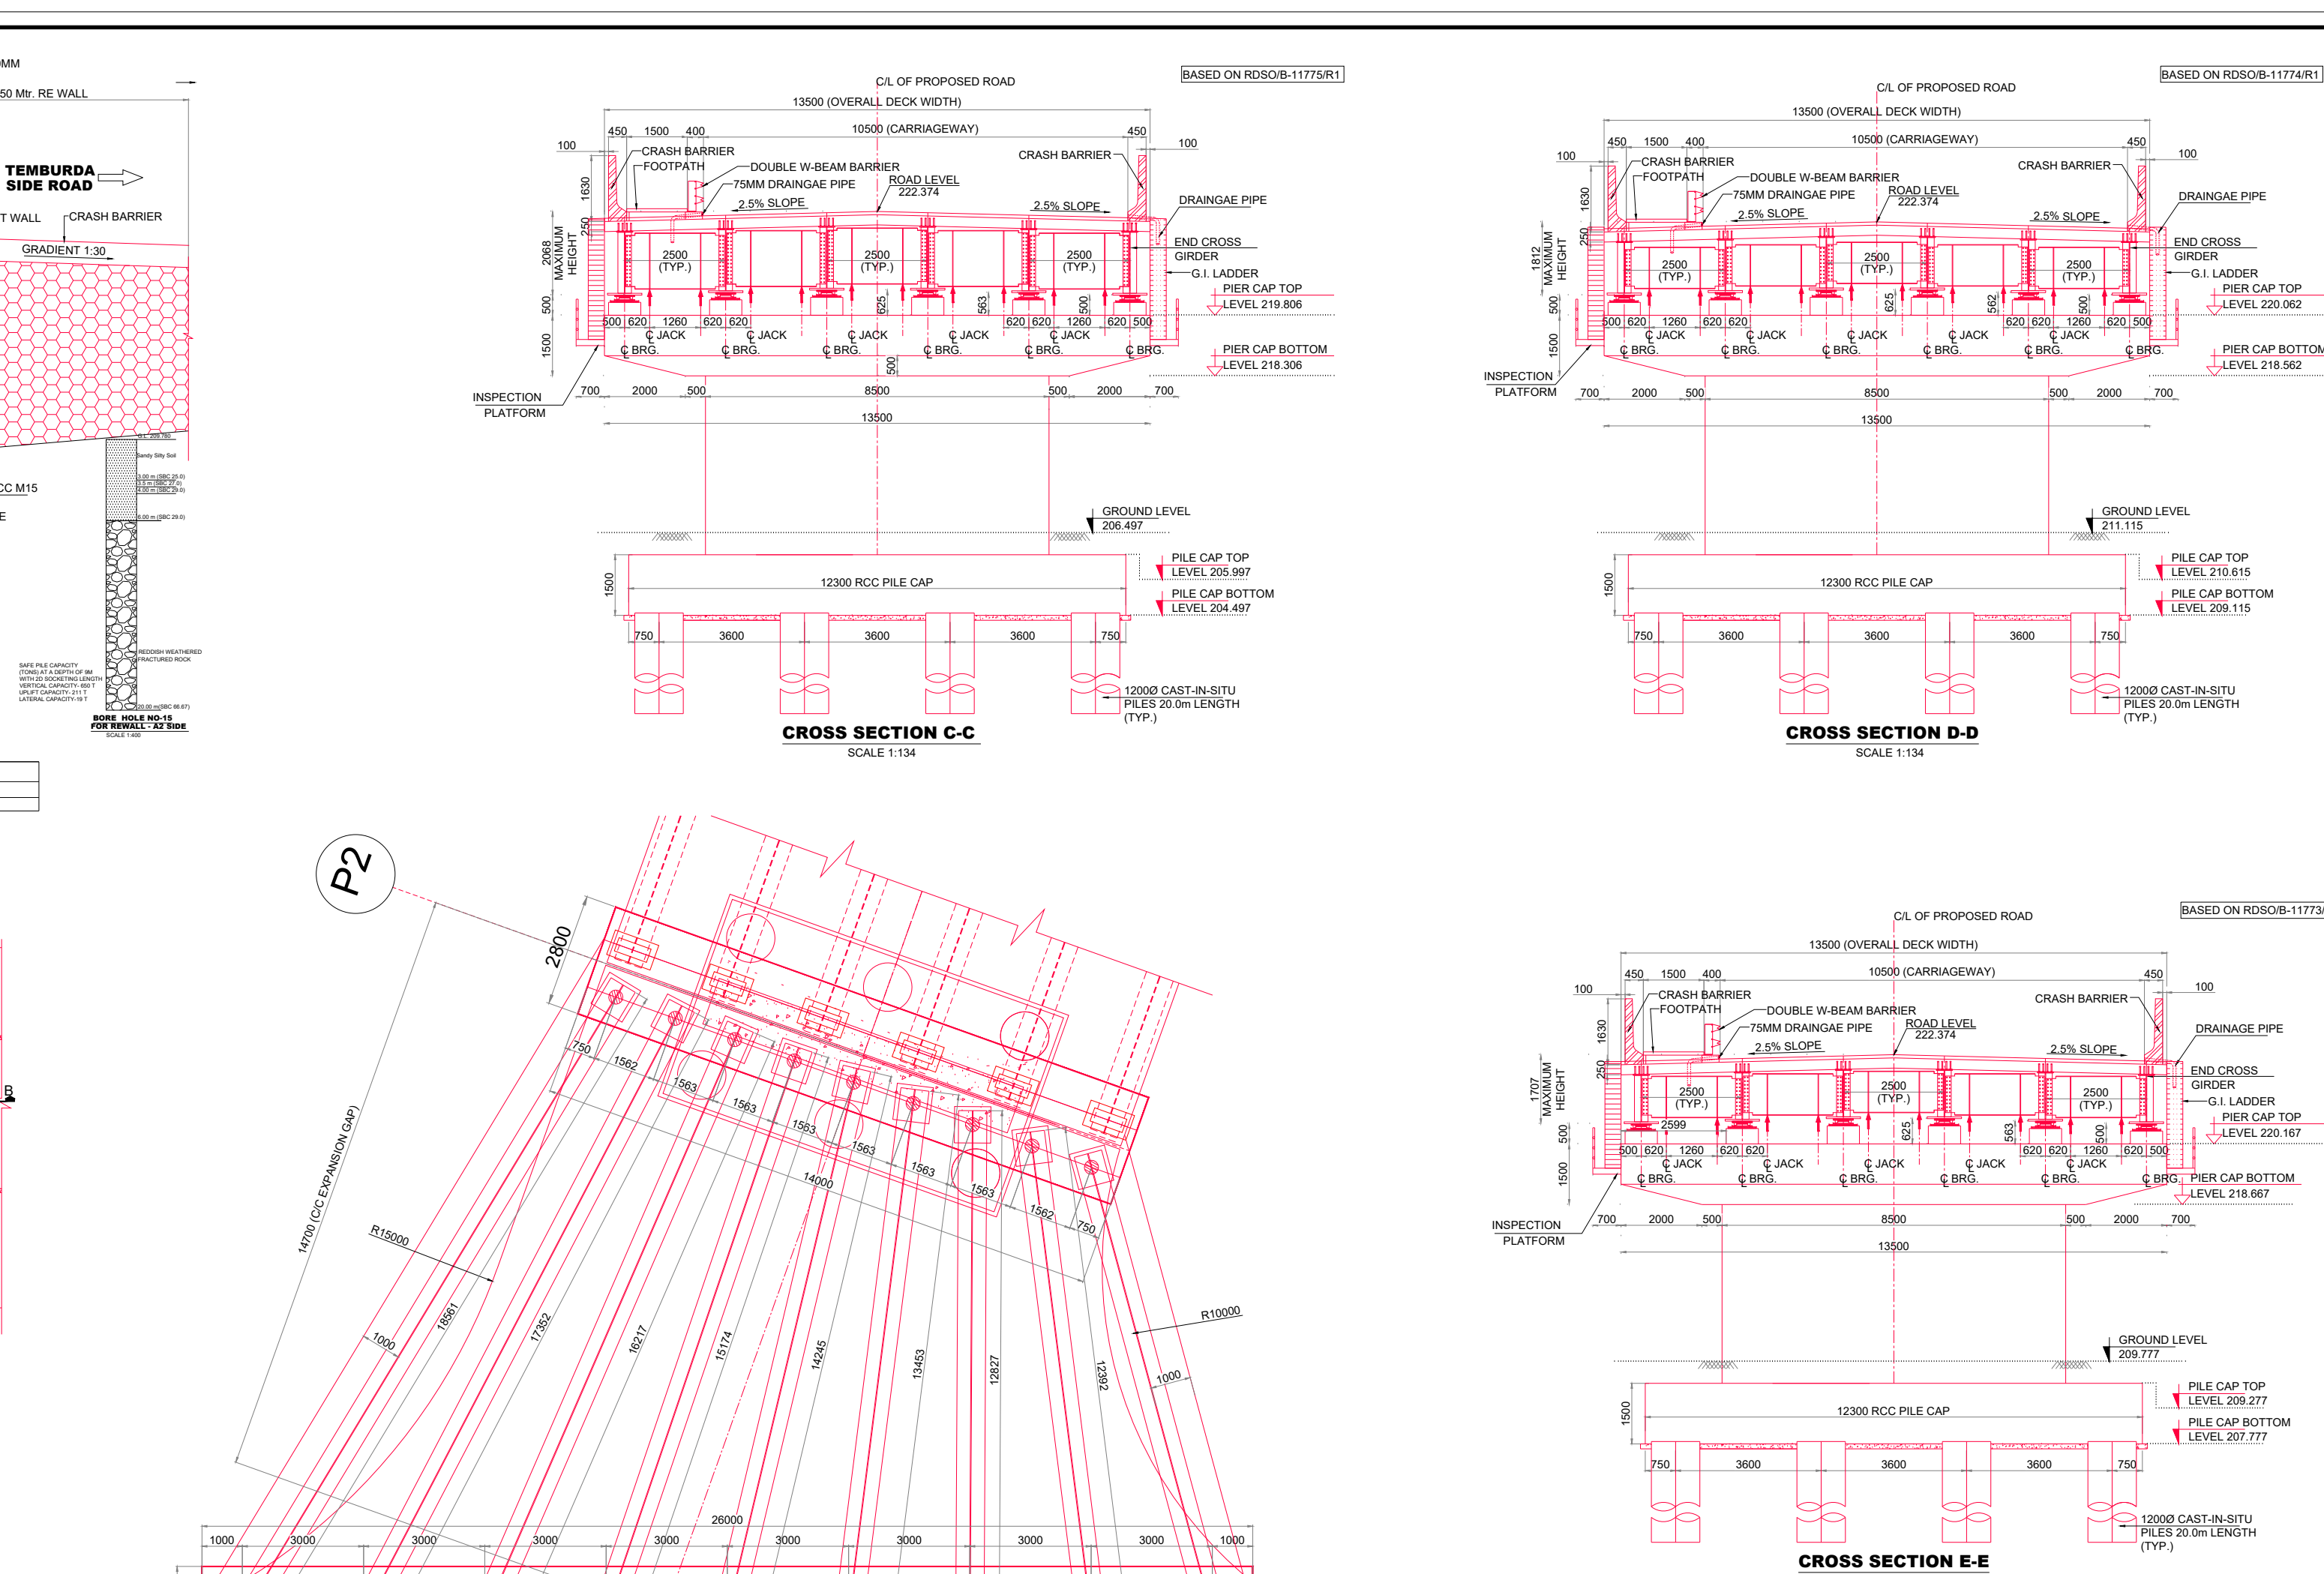

 P. K. MOHANI DIST. SANGREDDY DIST. (GARRA) DIST. (TANGA)	NAGPUR DIVISION	
	L - XING NO.25 ON CR/LY KM. NO. 819.562 BETWEEN ASHPAL - TEMBURDA	
	TITLE :- GENERAL ARRANGEMENT DRAWING OF PROPOSED 3 LANE ROAD OVER BRIDGE IN LIEU OF LEVEL CROSSING GATE NO. 25 @ KM. NO. 819.562 BETWEEN (NAGRI STN.-WARORA STN.) SPAN ARRANGEMENT: FOR ROAD SIDE, 5X36M (C.G.) & FOR RLY SIDE, 1X14 F.G. RIDGER-4X24 (C.G.) + 1X30 (C.G.) + 2X24 (C.G.)	
	PINK BOOK ITEM NO. - 212 OF 2019-20	
	DRAWING NO.	CONSULTANT: LKT / CR / WD / LC-25 / GAD-1 CONSTRUCTION: GM(E)-RSP-3004-ROB HEADQUARTERS:
SCALE: -		AS SHOWN